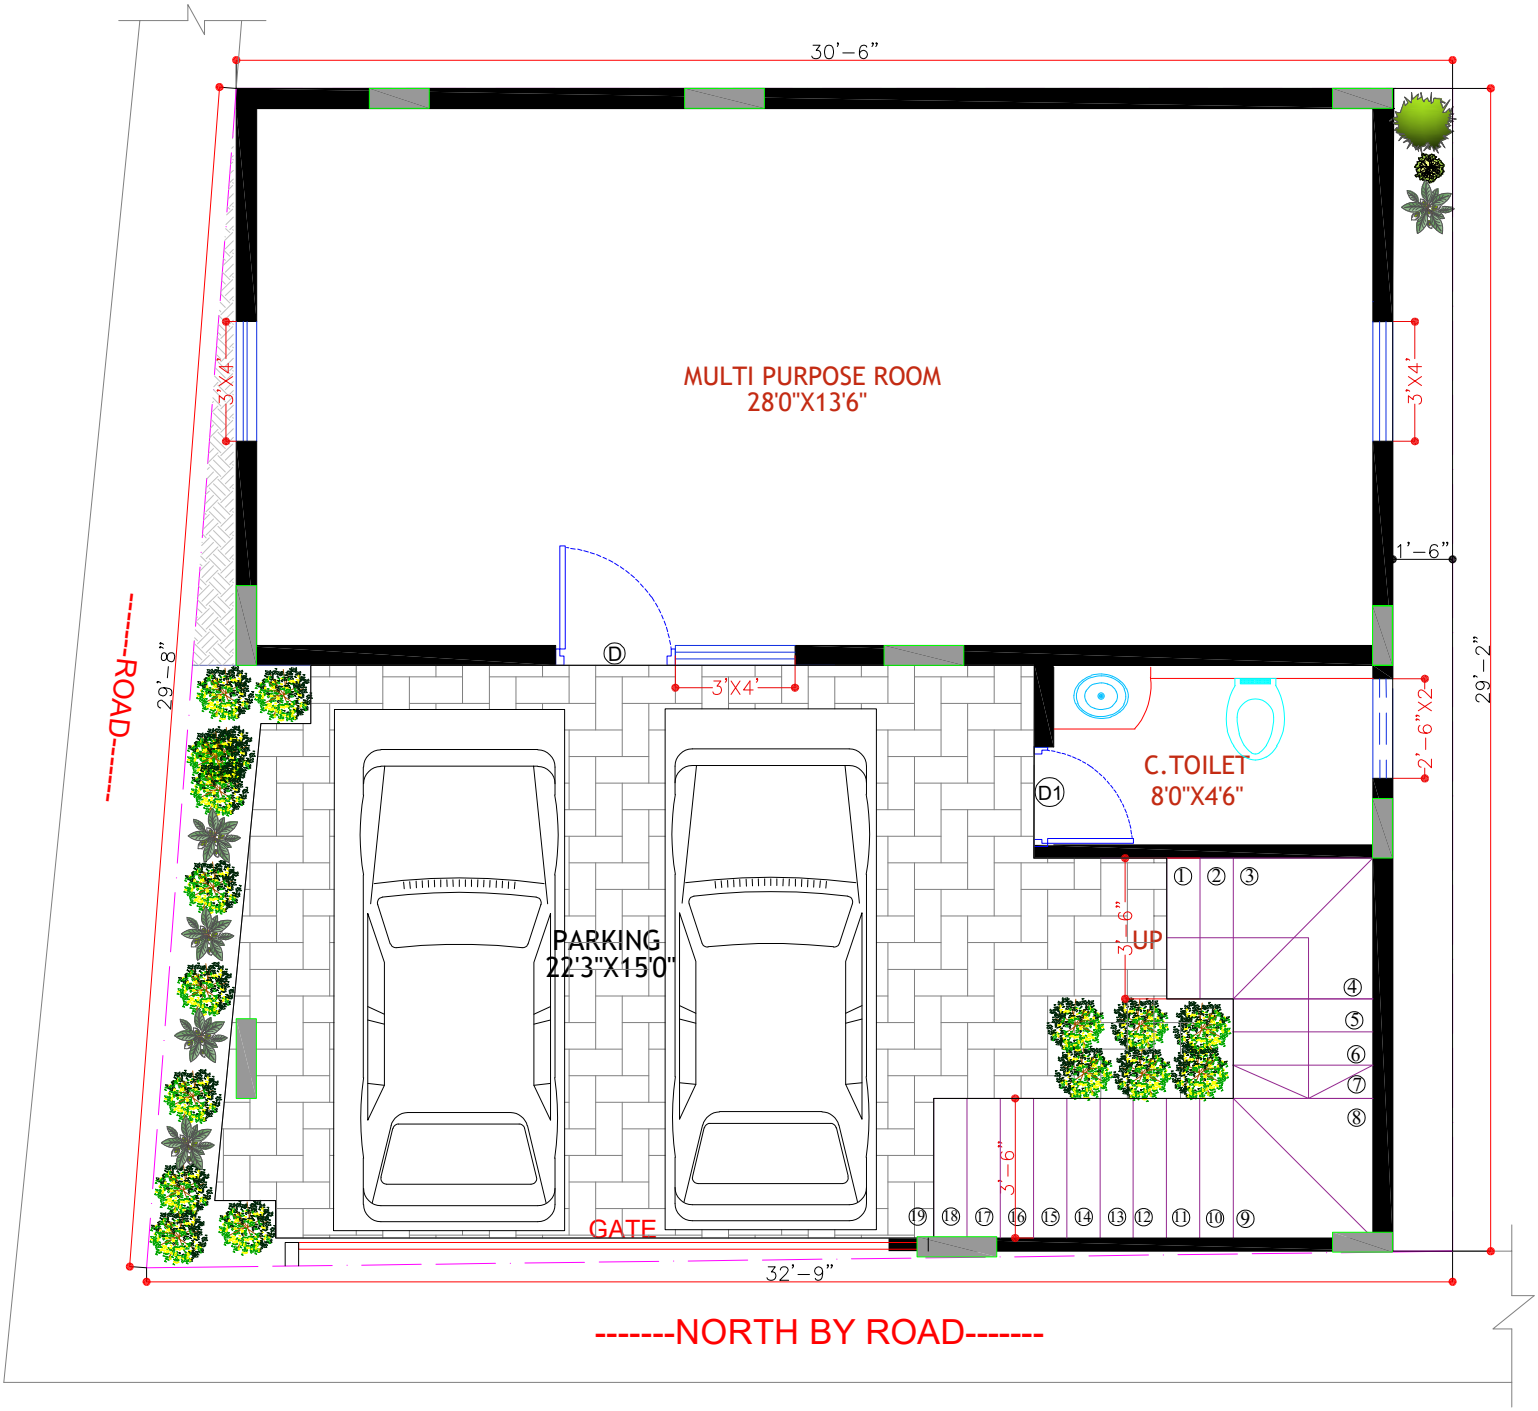

CLIENT:	Mr.Purushotham	NOTES: 01. ALL DIMENSIONS ARE IN INCHES & LEVELS ARE IN FEET. 02. DO NOT SCALE THE DRG. FOLLOW WRITTEN DIMENSIONS ONLY.		REVISIONS				ORIENTATION:	COPY RIGHT	THIS DRAWING IS THE PROPERTY OF HOUSE CONSTRUCT AND NOT TO BE USED OR COPIED WITHOUT THEIR PRIOR CONSENT OR APPROVAL				PRIME CONSULTANTS	HOUSE- CONSTRUCT DELIVERING THE BEST !
				ISSUED TO TO CLIENT	NO.	DATE	BY	S E W N	DRAWN	PREETHI	CHECKED	AMAN			
PROJECT:	PROPOSED RESIDENCE FOR Mr. PURUSHOTHAM AT BENGALURU	TITLE :	GROUND FLOOR PLAN						DATE	23.12.2024	SHEET	1 OF 1			
									JOB NO.		SCALE	N.T.S			
									DRG. NO.		REV. NO.	R3		STATUS :	FOR APPROVAL ONLY

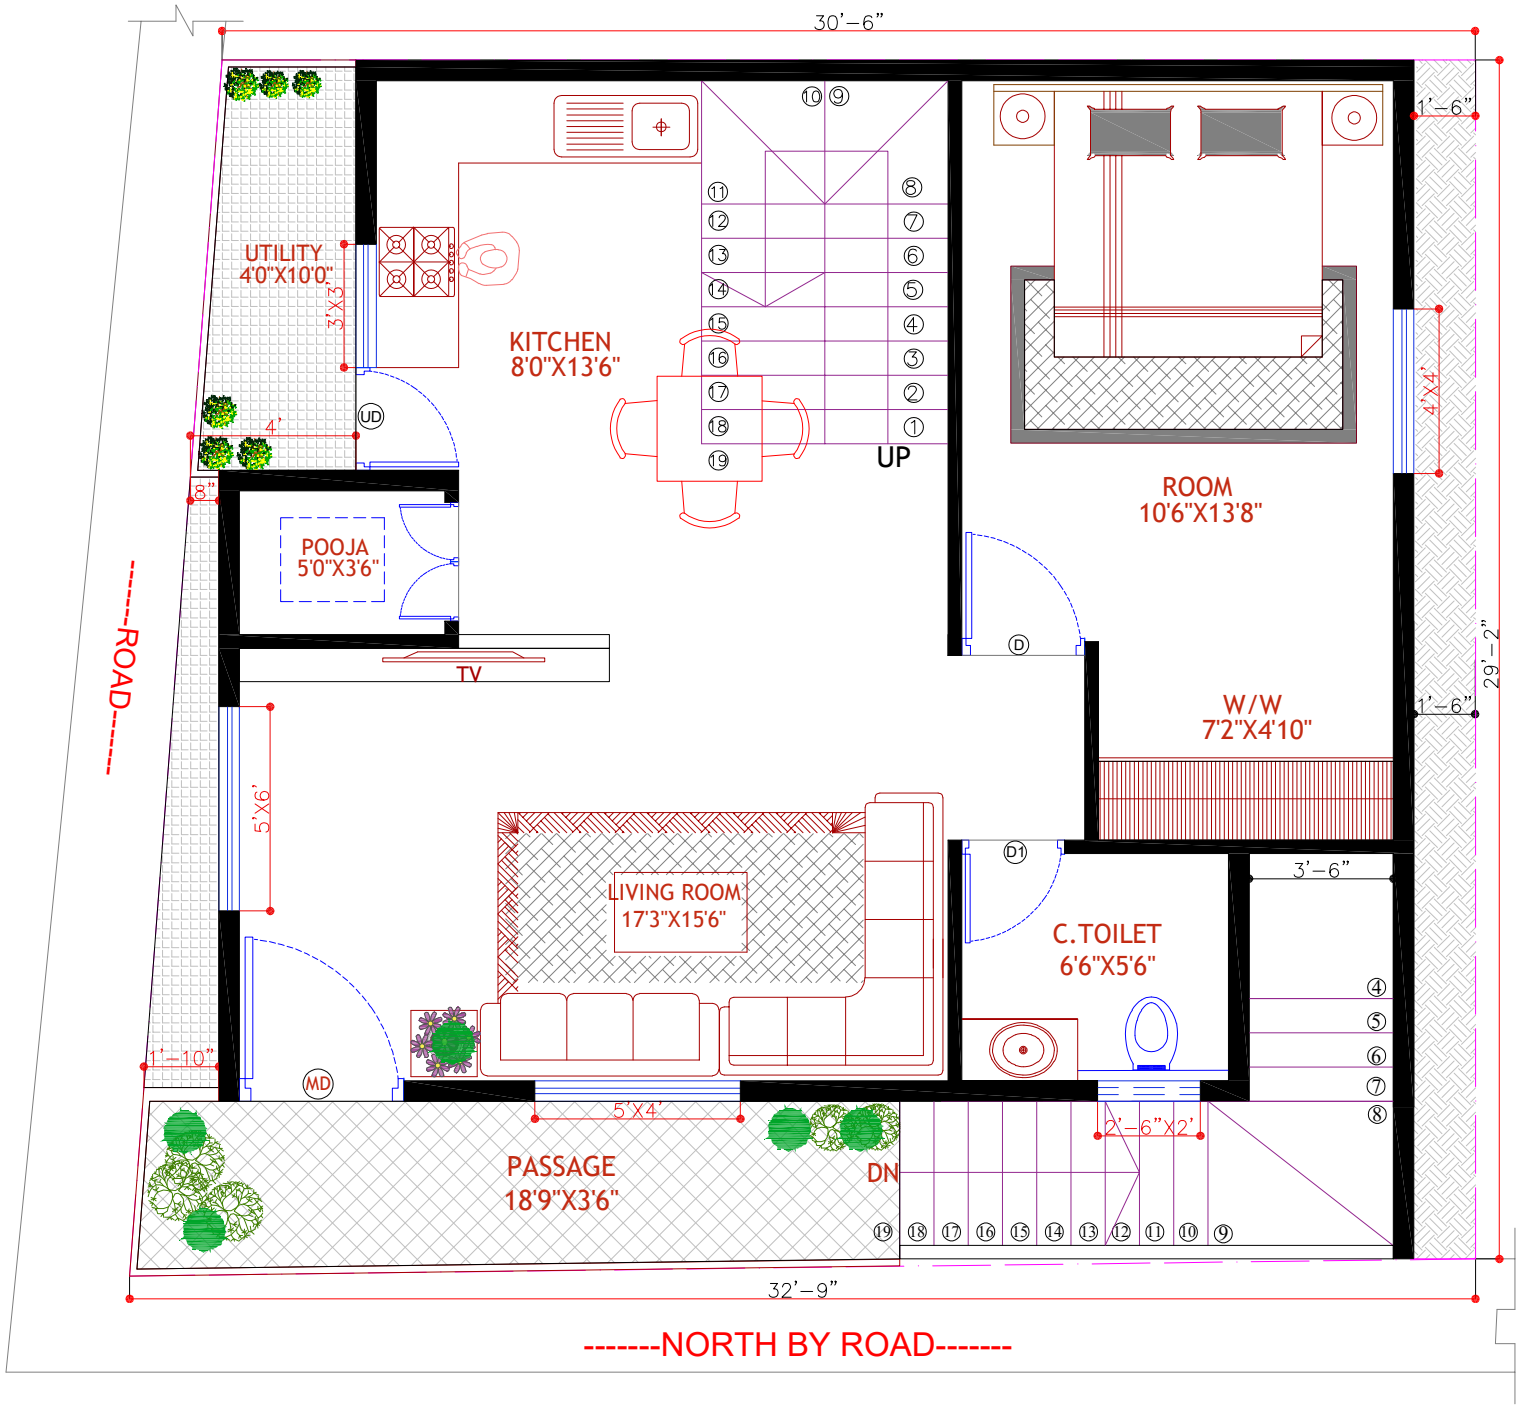

CLIENT:	Mr.Purushotham	NOTES: 01. ALL DIMENSIONS ARE IN INCHES & LEVELS ARE IN FEET. 02. DO NOT SCALE THE DRG. FOLLOW WRITTEN DIMENSIONS ONLY.		REVISIONS				ORIENTATION:	COPY RIGHT	THIS DRAWING IS THE PROPERTY OF HOUSE CONSTRUCT AND NOT TO BE USED OR COPIED WITHOUT THEIR PRIOR CONSENT OR APPROVAL				PRIME CONSULTANTS	HOUSE- CONSTRUCT DELIVERING THE BEST !
				ISSUED TO	NO.	DATE	BY	S E W N							
				TO CLIENT					DRAWN	PREETHI	CHECKED	AMAN			
PROJECT:	PROPOSED RESIDENCE FOR Mr. PURUSHOTHAM AT BENGALURU	TITLE :	FIRST FLOOR PLAN						DATE	23.12.2024	SHEET	1 OF 1			
									JOB NO.		SCALE	N.T.S			
									DRG. NO.		REV. NO.	R3		STATUS :	FOR APPROVAL ONLY

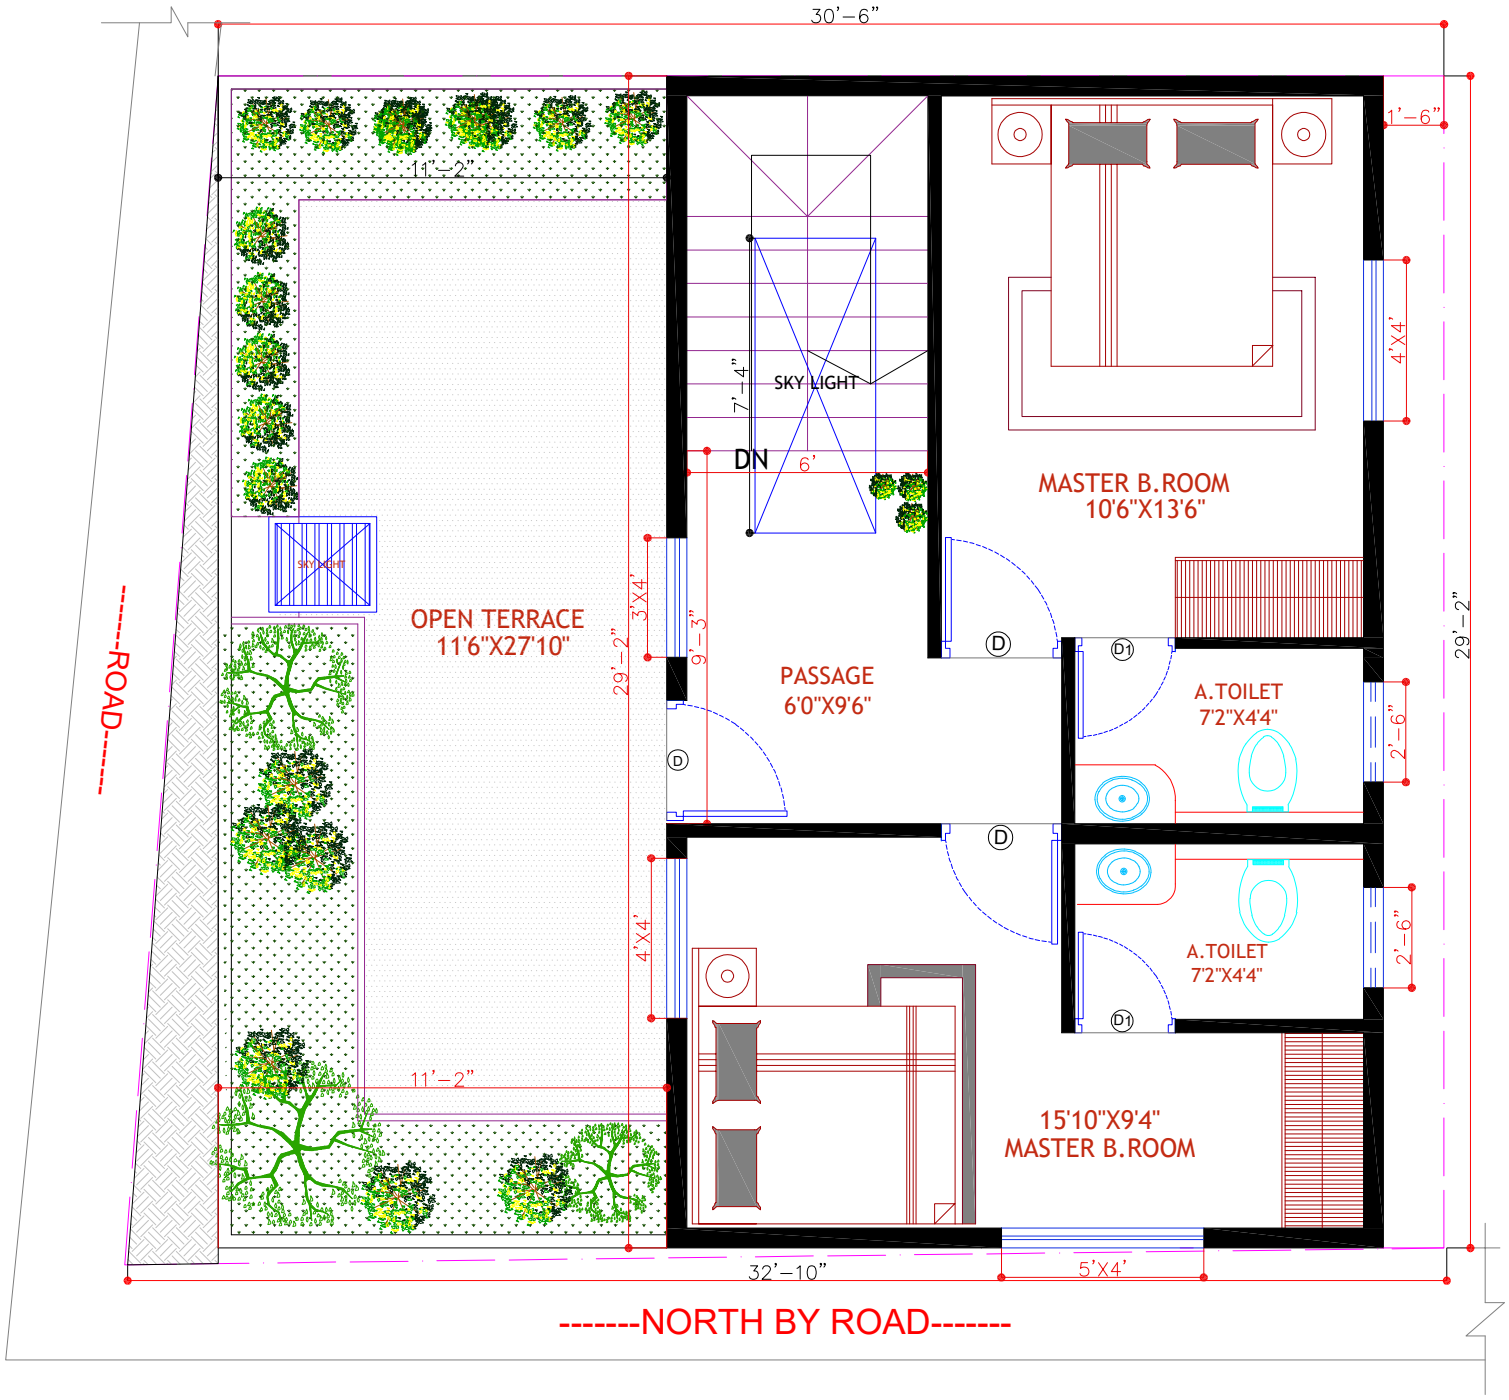

CLIENT:	Mr.Purushotham	NOTES: 01. ALL DIMENSIONS ARE IN INCHES & LEVELS ARE IN FEET. 02. DO NOT SCALE THE DRG. FOLLOW WRITTEN DIMENSIONS ONLY.		REVISIONS				ORIENTATION:	COPY RIGHT	THIS DRAWING IS THE PROPERTY OF HOUSE CONSTRUCT AND NOT TO BE USED OR COPIED WITHOUT THEIR PRIOR CONSENT OR APPROVAL			PRIME CONSULTANTS	HOUSE- CONSTRUCT DELIVERING THE BEST !	
				ISSUED TO	NO.	DATE	BY	S E W N							
				TO CLIENT					DRAWN	PREETHI	CHECKED	AMAN			
PROJECT:	PROPOSED RESIDENCE FOR Mr. PURUSHOTHAM AT BENGALURU	TITLE :	TERRACE FLOOR PLAN						DATE	23.12.2024	SHEET	1 OF 1			
									JOB NO.		SCALE	N.T.S			
									DRG. NO.		REV. NO.	R3	STATUS :	FOR APPROVAL ONLY	