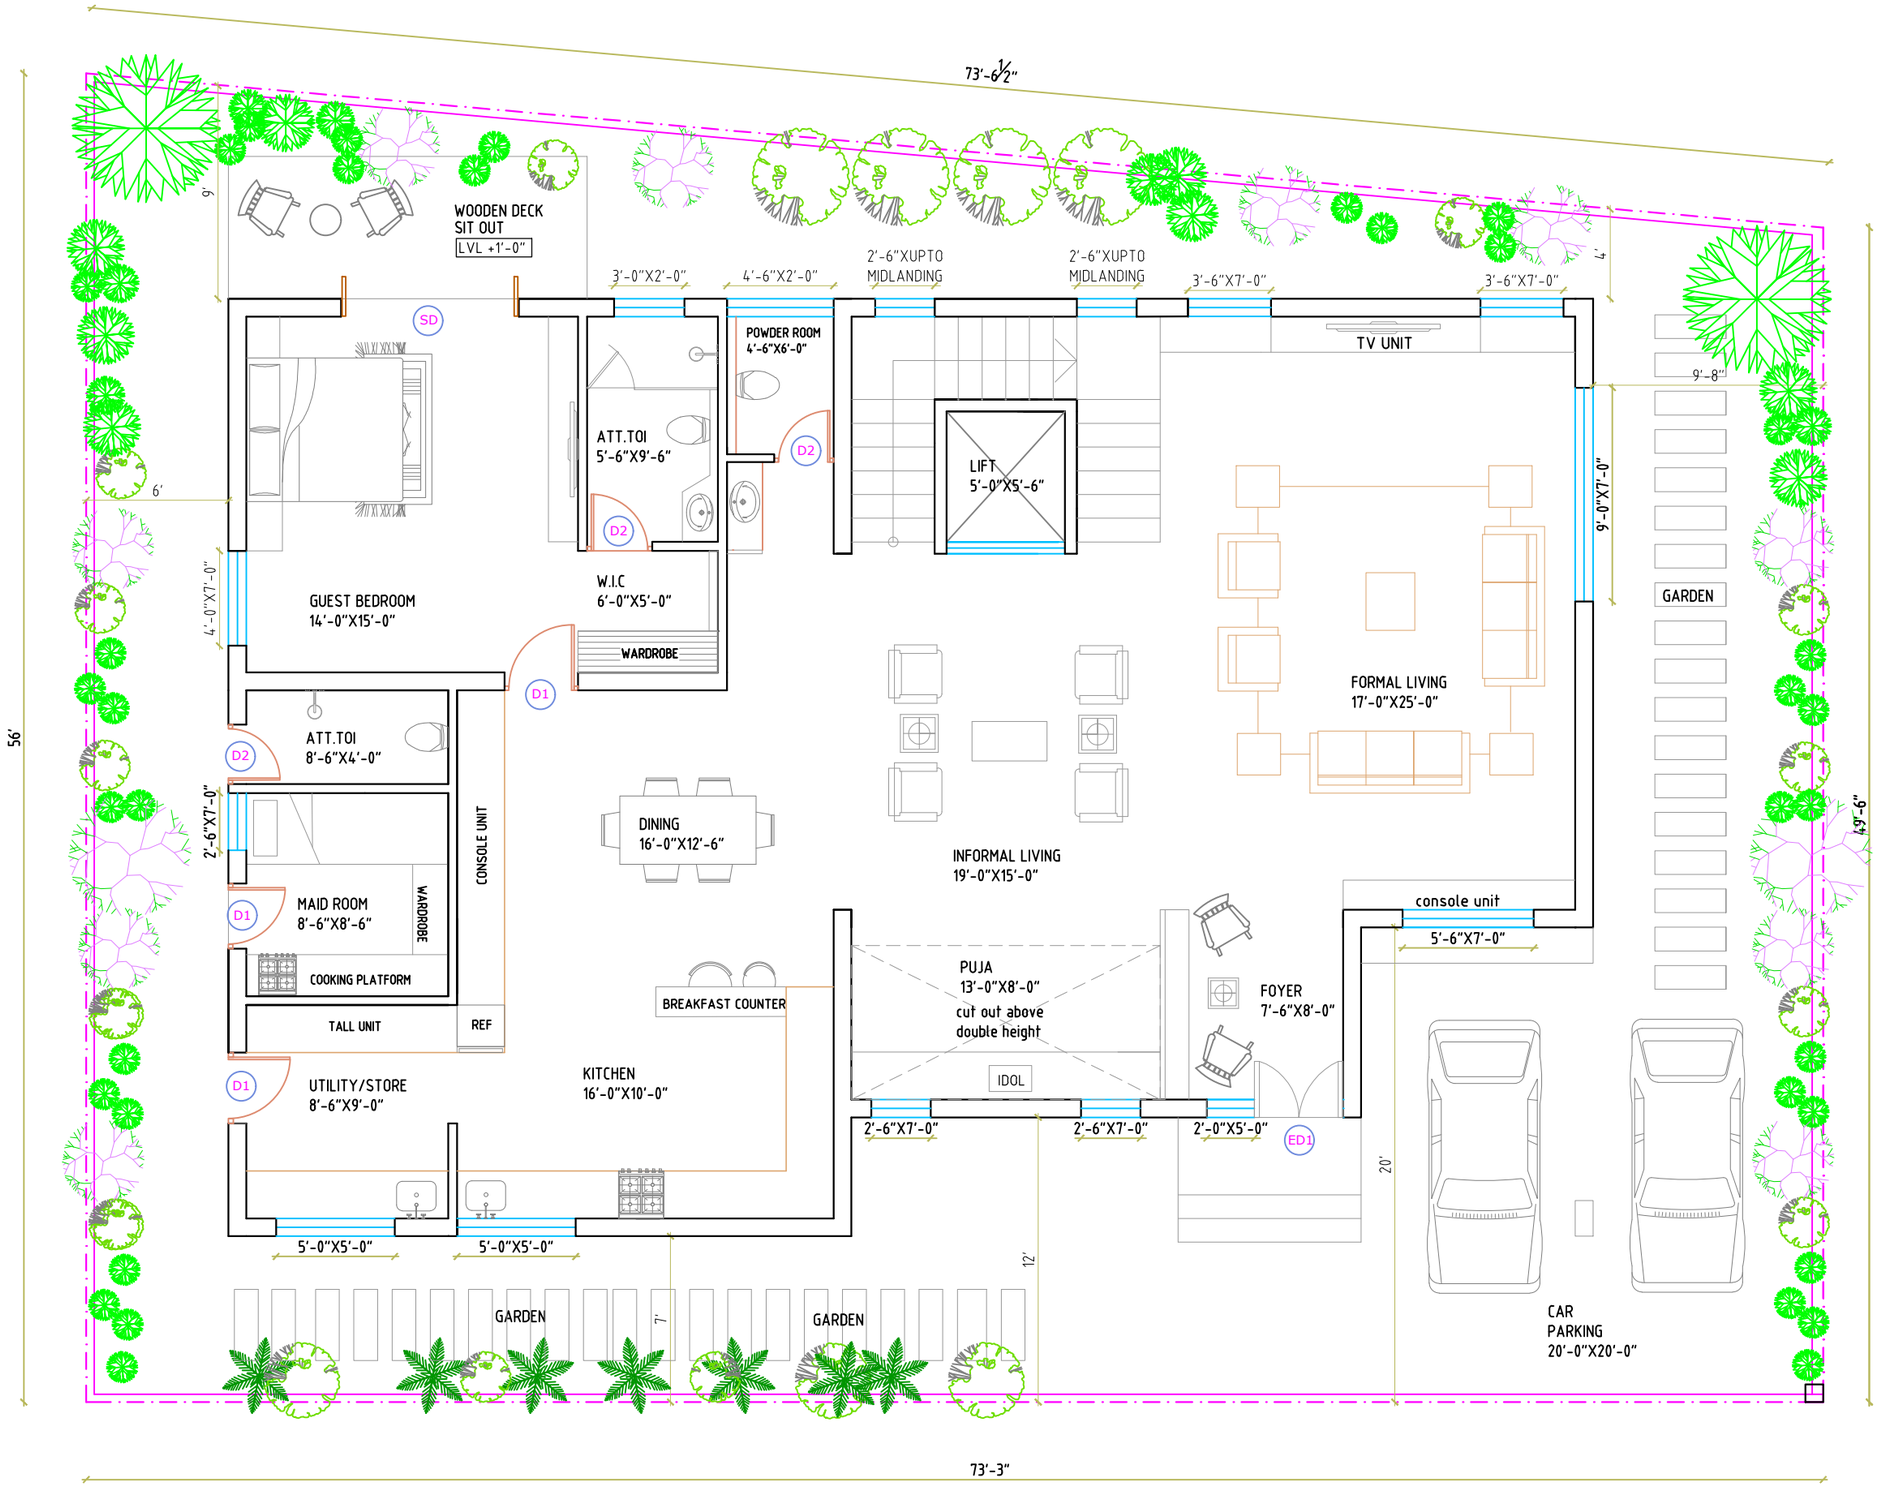

CLIENT:	Mr. ANKITH JAIN		
PROJECT:	PROPOSED RESIDENCE FOR Mr. ANKITH JAIN AT BANGALORE.	TITLE :	GROUND FLOOR PLAN

NOTES:
01. ALL DIMENSIONS ARE IN INCHES & LEVELS ARE IN FEET.
02. DO NOT SCALE THE DRG. FOLLOW WRITTEN DIMENSIONS ONLY.

REVISIONS

ISSUED TO	NO.	DATE	BY
TO CLIENT	01	28.09.2023	.....
TO CLIENT	01	06.10.2023	.....
TO CLIENT	01	16.10.2023	.....
TO CLIENT	01	22.10.2023	.....
TO CLIENT	01	25.10.2023	.....

ORIENTATION:

W S N E

COPY RIGHT: THIS DRAWING IS THE PROPERTY OF HOUSE CONSTRUCT AND NOT TO BE USED OR COPIED WITHOUT THEIR PRIOR CONSENT OR APPROVAL

DRAWN	AMAN	CHECKED	AMAN
DATE	28.09.2023	SHEET	1 OF 1
JOB NO.	NO.RFS.:- 26	SCALE	N.T.S
DRG. NO.	.....	REV. NO.	R4

PRIME CONSULTANTS

HOUSE-CONSTRUCT
DELIVERING THE BEST!

STATUS : FOR APPROVAL ONLY

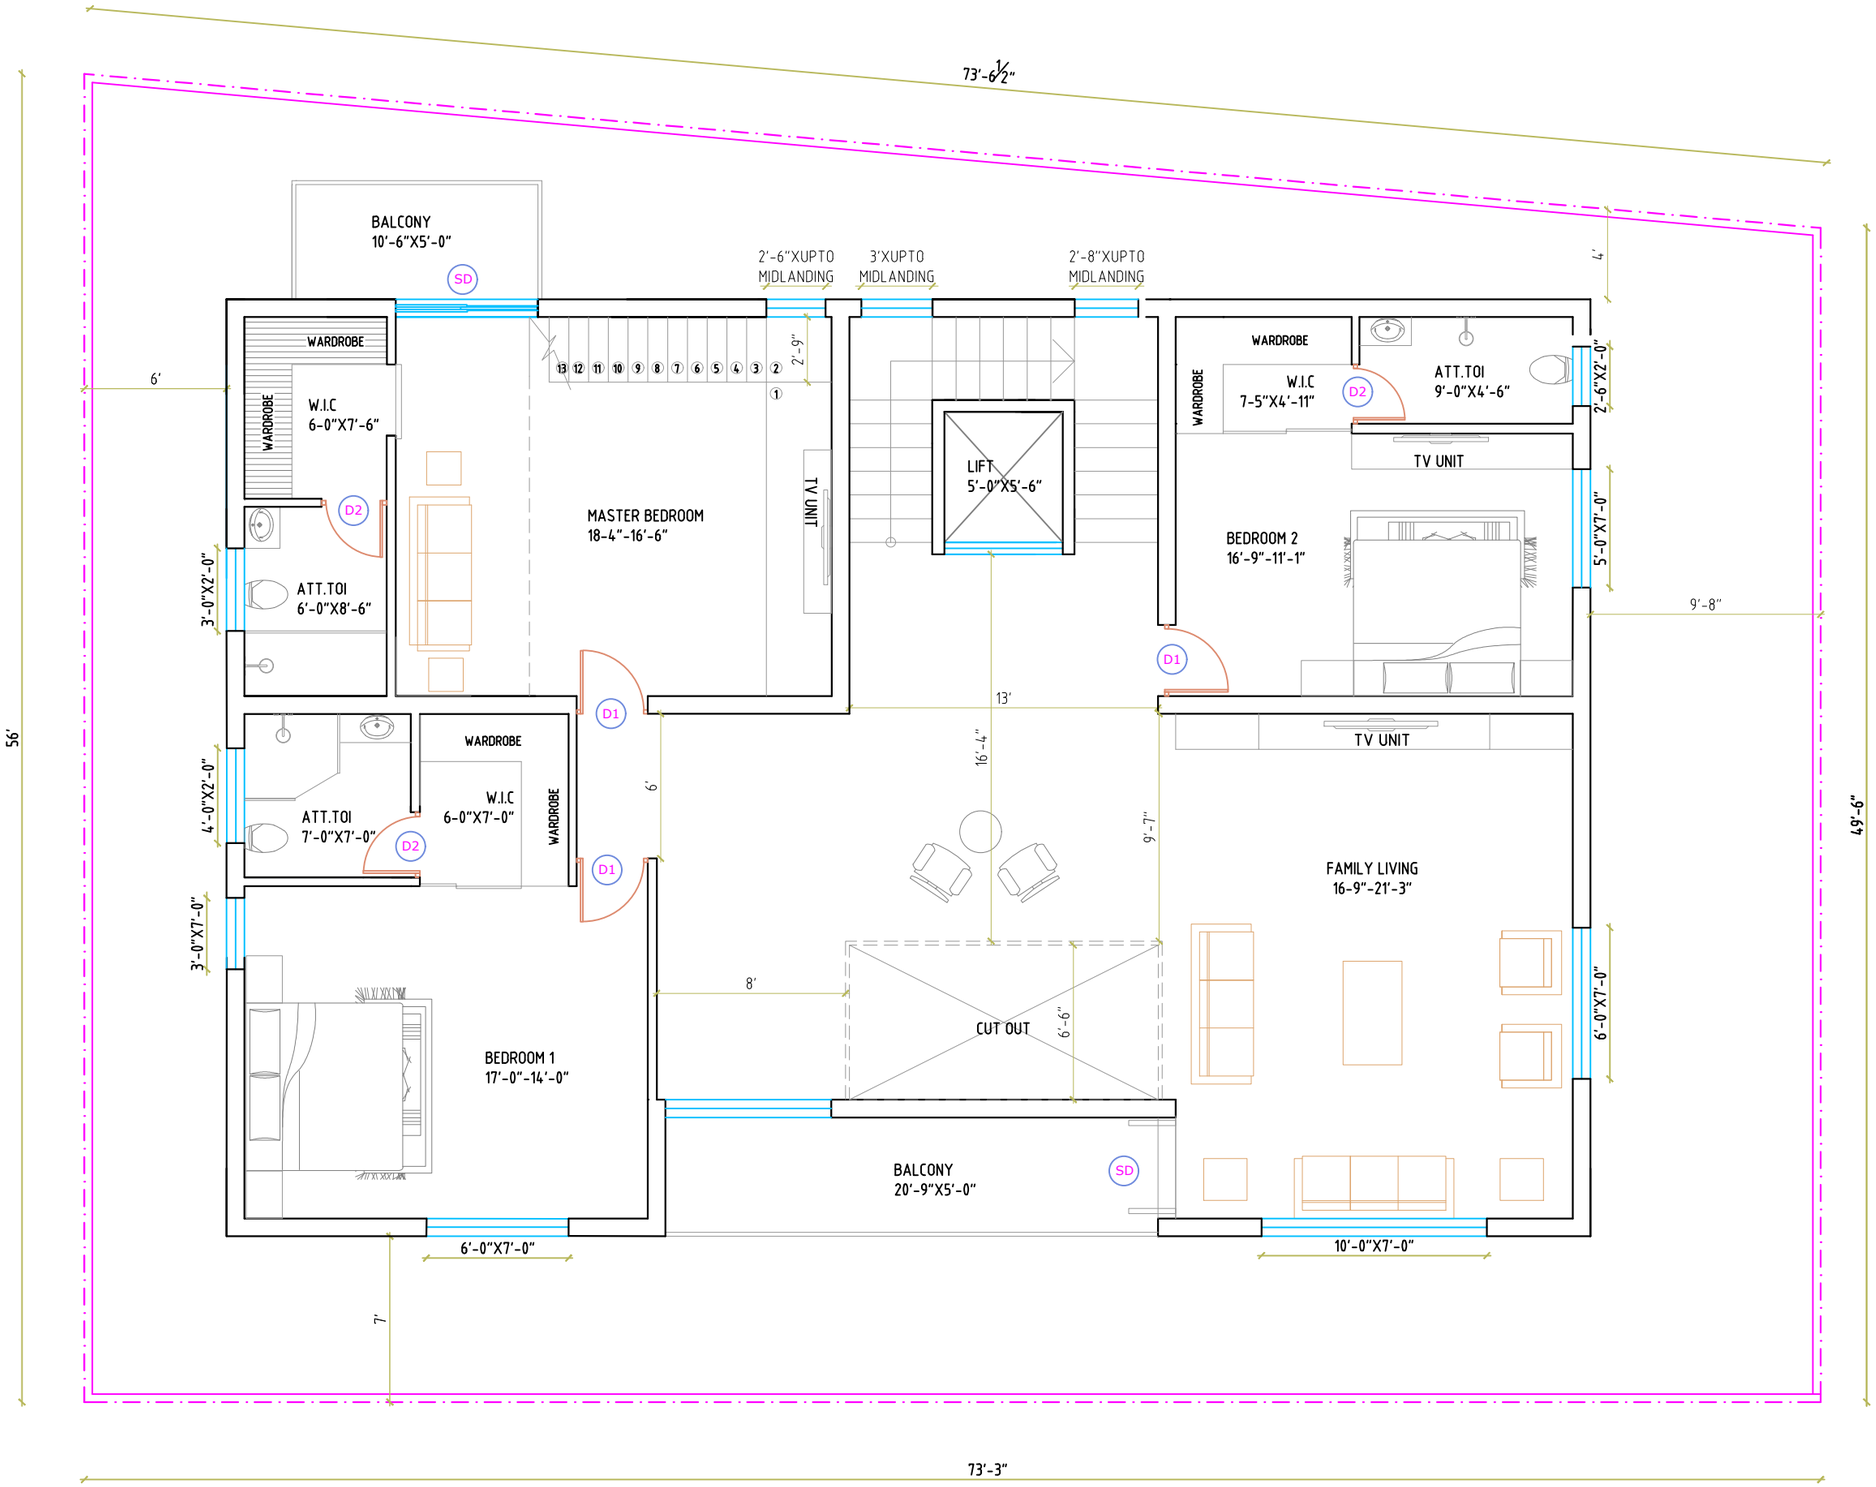

CLIENT:	Mr. ANKITH JAIN		
PROJECT:	PROPOSED RESIDENCE FOR Mr. ANKITH JAIN AT BANGALORE.		

NOTES:
01. ALL DIMENSIONS ARE IN INCHES & LEVELS ARE IN FEET.
02. DO NOT SCALE THE DRG. FOLLOW WRITTEN DIMENSIONS ONLY.

TITLE : FIRST FLOOR PLAN

REVISIONS

ISSUED TO	NO.	DATE	BY
TO CLIENT	01	28.09.2023	.....
TO CLIENT	01	06.10.2023	.....
TO CLIENT	01	16.10.2023	.....
TO CLIENT	01	22.10.2023	.....
TO CLIENT	01	25.10.2023	.....

ORIENTATION: W S N E

COPY RIGHT: THIS DRAWING IS THE PROPERTY OF HOUSE CONSTRUCT AND NOT TO BE USED OR COPIED WITHOUT THEIR PRIOR CONSENT OR APPROVAL

DRAWN	AMAN	CHECKED	AMAN
DATE	28.09.2023	SHEET	1 OF 1
JOB NO.	NO.RFS.:- 26	SCALE	N.T.S
DRG. NO.	.....	REV. NO.	R4

PRIME CONSULTANTS: HOUSE-CONSTRUCT DELIVERING THE BEST!

STATUS : FOR APPROVAL ONLY

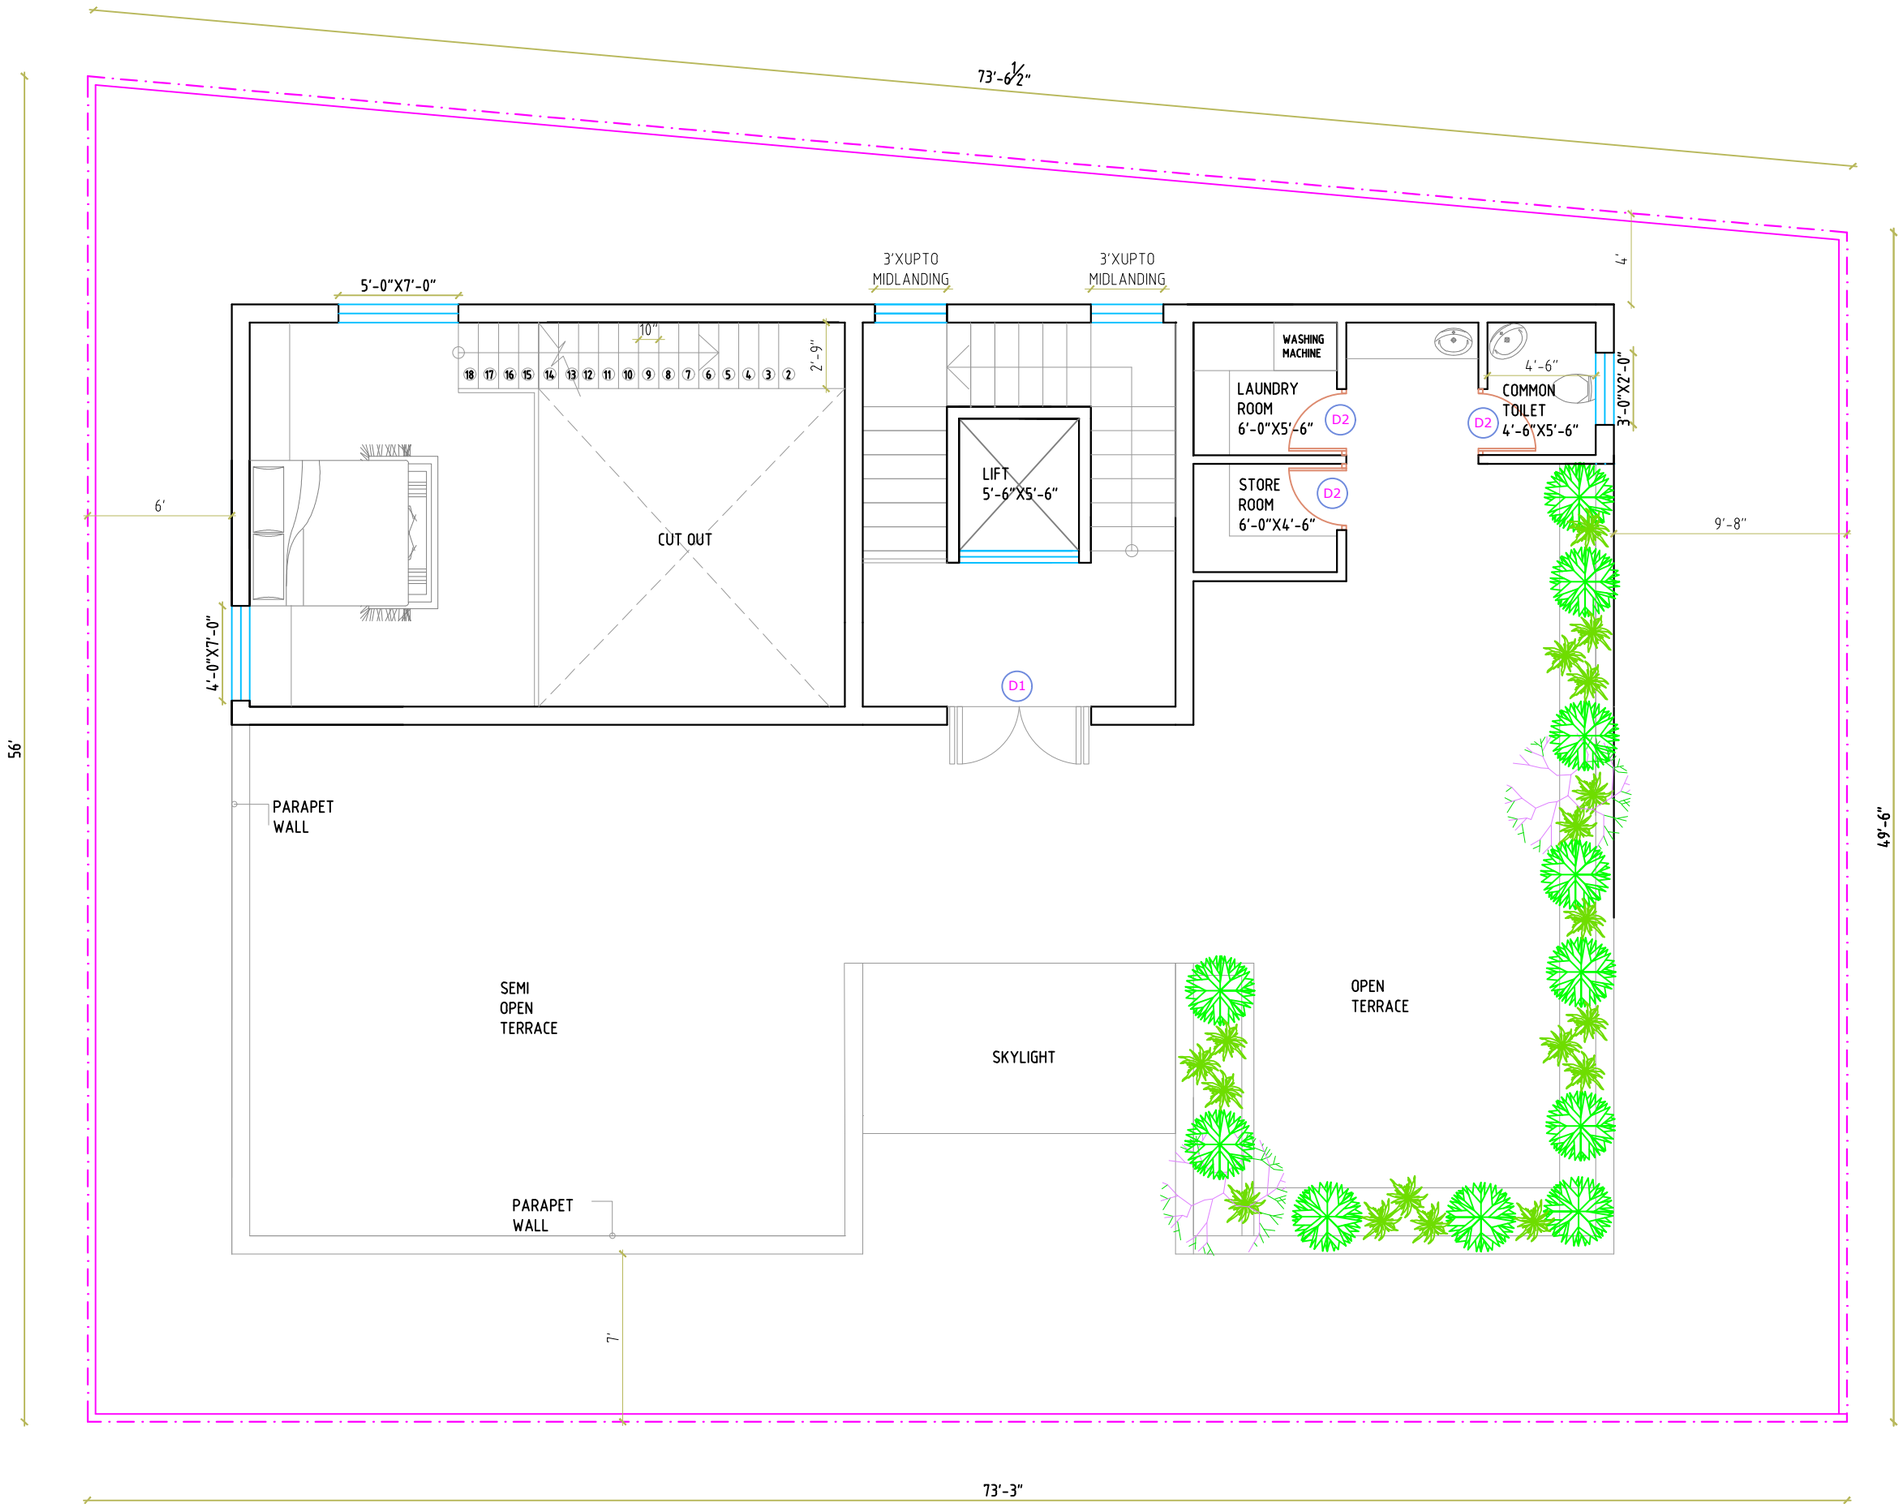

CLIENT:	Mr. ANKITH JAIN	NOTES: 01. ALL DIMENSIONS ARE IN INCHES & LEVELS ARE IN FEET. 02. DO NOT SCALE THE DRG. FOLLOW WRITTEN DIMENSIONS ONLY.		REVISIONS				ORIENTATION:	COPY RIGHT	THIS DRAWING IS THE PROPERTY OF HOUSE CONSTRUCT AND NOT TO BE USED OR COPIED WITHOUT THEIR PRIOR CONSENT OR APPROVAL			PRIME CONSULTANTS	HOUSE-CONSTRUCT DELIVERING THE BEST!
				ISSUED TO	NO.	DATE	BY	W S N E					
				TO CLIENT	01	28.09.2023	.....						
				TO CLIENT	01	06.10.2023	.....						
PROJECT:	PROPOSED RESIDENCE FOR Mr. ANKITH JAIN AT BANGALORE.	TITLE :	SECOND FLOOR PLAN	TO CLIENT	01	16.10.2023	.....		DRAWN	AMAN	CHECKED	AMAN	
				TO CLIENT	01	22.10.2023	.....		DATE	28.09.2023	SHEET	1 OF 1	
				TO CLIENT	01	25.10.2023	.....		JOB NO.	NO.RFS.:- 26	SCALE	N.T.S	
									DRG. NO.	.....	REV. NO.	R4	STATUS : FOR APPROVAL ONLY